KARTA ZAGOSPODAROWANIA DZIAŁKI

Działki nr 2834/9, 2834/8, 2834/11, obręb Siepraw

Identyfikator	120906_2.0003.2834/9 + 120906_2.0003.2834/8, 120906_2.0003.2834/11
Położenie	gm. Siepraw, powiat myślenicki, woj. małopolskie
Adres	brak adresu w granicach działki; najbliższe: Kardynała Franciszka Macharskiego 16, 32-447 Siepraw (19 m); Kardynała Franciszka Macharskiego 14, 32-447 Siepraw (22 m); Świętego Michała Archanioła 76, 32-447 Siepraw (30 m)
Projekt / wariant	**Dz. 2834/9 Siepraw** · Wariant 1
Data	27.10.2026

1857 m²
teren z połączonych działek


1868 m²
teren inwestycji

12,3%
zabudowa (teren inwestycji)

81,0%
biologicznie czynna (ok.)

2
budynki · 231 m²

✓ brak
kontrola odległości

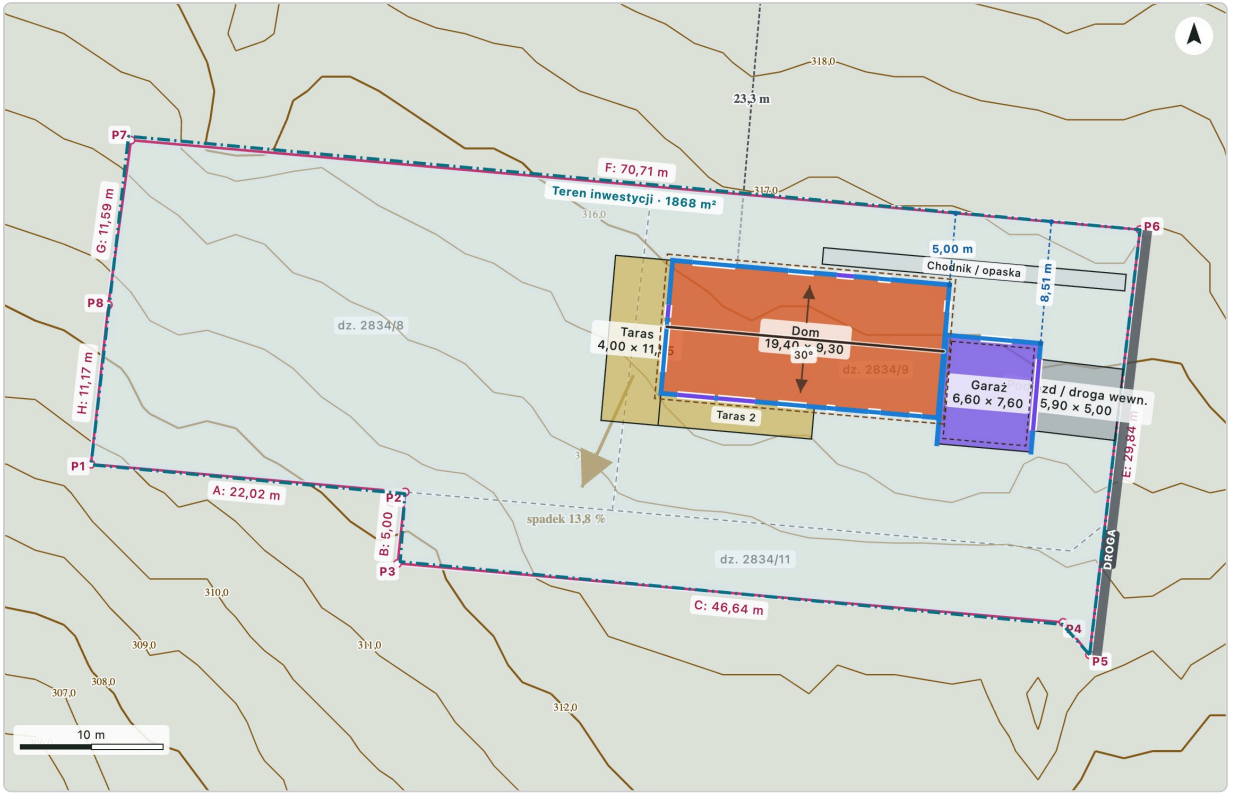


Kontrola odległości

✓ Wszystkie sprawdzane odległości są zachowane.

Plan miejscowy / WZ

✓ Wszystkie wpisane parametry (7) są spełnione.

Opracowanie poglądowe przygotowane w Planerze działki (planerdzialki.pl). Nie zastępuje mapy do celów projektowych ani projektu zagospodarowania działki – wymiary i odległości potwierdza projektant.

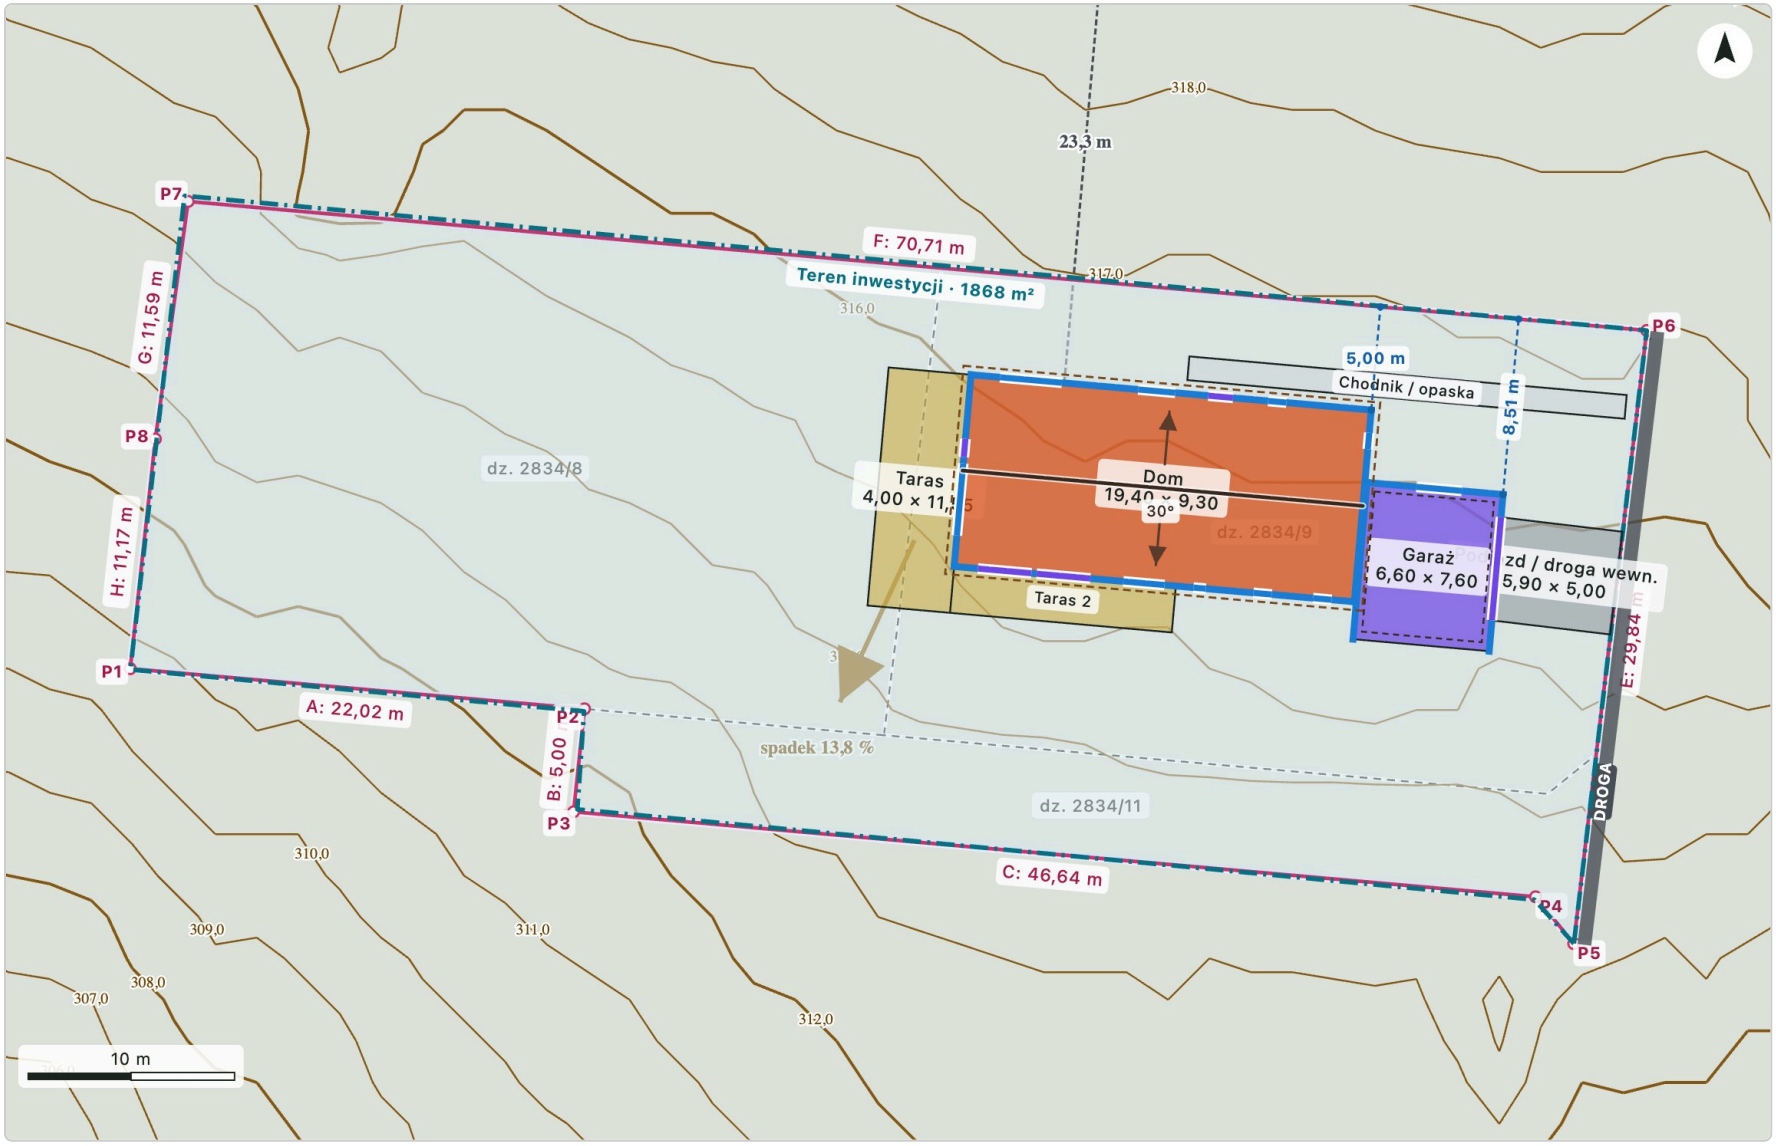

Plan zagospodarowania – cała działka · skala przy druku na A4 bez skalowania: ok. **1:300** · północ u góry

granica działki · Dom · Garaż · Teren inwestycji (obszar) · Podjazd / droga wewn. · Chodnik / opaska · Taras ×2

Teren inwestycji – punkty i kąty

Punkt	Kąt wewn.	Bok do następnego	Położenie
T1	48,7°	2,86 m (T1–T2)	narożnik działki P5
T2	222,7°	46,42 m (T2–T3)	wewnątrz działki
T3	91,4°	4,75 m (T3–T4)	wewnątrz działki
T4	268,7°	22,00 m (T4–T5)	granica B: 0,12 m od P2, 4,88 m od P3
T5	88,7°	23,04 m (T5–T6)	narożnik działki P1
T6	91,3°	70,91 m (T6–T7)	wewnątrz działki
T7	88,5°	29,84 m (T7–T1)	narożnik działki P6

Powierzchnia 1868,1 m², obwód 199,82 m. Odległości punktów na granicy mierzone wzdłuż granicy od narożników działki.

Bilans terenu

Pozycja	m²	% działki
Powierzchnia działki (z geometrii)	1856,8	100%
Teren inwestycji	**1868,1**	**100,61%**
W terenie inwestycji: zabudowa 230,6 m² (12,34%), utwardzenia 124,3 m² (6,65%), biologicznie czynna ok. 1513,2 m² (81,0%). Wiersze poniżej dotyczą całej działki.		
Powierzchnia zabudowy (budynki)	230,6	12,42%
Utwardzenia (podjazd, taras, chodniki...)	124,3	6,69%
Zagospodarowane razem	**354,8**	**19,11%**
Pozostaje biologicznie czynnej (ok.)	1501,9	80,89%

Kontrola odległości

✓ Wszystkie sprawdzane odległości są zachowane.

Wymóg	m
Ściana z oknami/drzwiami – granica	4,0
Ściana bez otworów – granica	3,0
Okap – granica działki (min.)	1,5
Okap – budynek 1,5 m od granicy lub w granicy (min.)	1,0
Budynek – budynek sąsiada (ppoż., orientacyjnie)	8,0

Pokazuję wymagania dotyczące obiektów z tego projektu.

Zgodność z planem miejscowym / WZ

Parametr	W projekcie	Wymóg	
Powierzchnia zabudowy	12,3 %	maks. 40,0 %	✓
Pow. biologicznie czynna	81,0 %	min. 40,0 %	✓
Intensywność zabudowy	0,12	maks. 40,00	✓
Wysokość: Dom	6,00 m	maks. 11,00 m	✓
Dach: Dom	dwuspadowy	dwu- lub wielospadowy	✓
Kąt dachu: Dom	30°	30–45°	✓
Elewacja frontowa: Dom	9,88 m	maks. 16,00 m	✓

Wskaźniki liczone dla terenu inwestycji (1868 m²). Parametry wpisane ręcznie z planu miejscowego lub decyzji WZ – sprawdź je z dokumentem.

Budynki – parametry, ściany i odległości od granic

Budynek	Wymiary	Pow. zabud.	Kond.	Wysokość	Dach	Kalenica
Dom	19,40 × 9,30 m	180,4 m²	1	6,0 m	dwuspadowy, 30°	wschód – zachód
Garaż	6,60 × 7,60 m	50,2 m²	–	3,0 m	płaski	–

Budynek	Ściana	Dł. [m]	Rodzaj	Najbliższa granica	Odl. [m]	Wymagane	
Dom	1	19,40	okna/drzwi	F	5,00	4,0	✓
	2	9,30	okna/drzwi	F	5,00	4,0	✓
	3	19,40	okna/drzwi	C	13,43	4,0	✓
	4	9,30	okna/drzwi	F	5,01	4,0	✓
Garaż	1	6,60	okna/drzwi	F	8,51	4,0	✓
	2	7,60	okna/drzwi	F	8,51	4,0	✓
	3	6,60	bez otworów	C	11,62	3,0	✓
	4	7,60	okna/drzwi	F	8,51	4,0	✓

Zestawienie obiektów

Obiekt	Rodzaj	Wymiary	Pow. [m²]	Najbliższa granica	Odl. [m]
Dom	Dom	19,40 × 9,30 m	180,4	F	5,00
Garaż	Garaż	6,60 × 7,60 m	50,2	E	5,72
Podjazd / droga wewn.	Podjazd / droga wewn.	5,90 × 5,00 m	29,5	E	0,02
Chodnik / opaska	Chodnik / opaska	21,20 × 1,15 m	24,4	E	0,56
Taras	Taras	4,00 × 11,55 m	46,2	F	5,01
Taras 2	Taras	10,75 × 2,25 m	24,2	C	11,18

Działki w projekcie

Działka	Obręb	Identyfikator	Pow. [m²]	Rola
2834/9	Siepraw	120906_2.0003.2834/9	776	działka główna
2834/8	Siepraw	120906_2.0003.2834/8	832	w terenie inwestycji
2834/11	Siepraw	120906_2.0003.2834/11	249	w terenie inwestycji

Granice terenu (obrys) i współrzędne PL-1992

Granica	Długość [m]	Punkt	X (PL-1992)	Y (PL-1992)	Uwagi
A (P1–P2)	22,02	P1	227937.00	569521.89	
B (P2–P3)	5,00	P2	227935.06	569543.82	
C (P3–P4)	46,64	P3	227930.08	569543.30	
D (P4–P5)	2,91	P4	227925.97	569589.75	
E (P5–P6)	29,84	P5	227923.71	569591.59	droga
F (P6–P7)	70,71	P6	227953.34	569595.12	
G (P7–P8)	11,59	P7	227959.58	569524.68	
H (P8–P1)	11,17	P8	227948.10	569523.10	

Opracowanie poglądowe z planera działki. Granice: GUGiK ULDK, podkład: ortofotomapa GUGiK. Dokładność granic zależy od danych ewidencyjnych, a wiążąca jest mapa do celów projektowych. Wymagane odległości według rozporządzenia o warunkach technicznych (wersja z 2002 r., §12, §31, §36) do potwierdzenia przez projektanta. Długości tras liczone po osi narysowanej linii, bez podejść pionowych.

Gdzie załatwisz sprawy dla tej działki

Urząd	Nazwa	Po co
Adres działki	brak adresu w granicach działki	najbliższe adresy: Kardynała Franciszka Macharskiego 16, 32-447 Siepraw (19 m); Kardynała Franciszka Macharskiego 14, 32-447 Siepraw (22 m); Świętego Michała Archanioła 76, 32-447 Siepraw (30 m) – numer porządkowy nadaje gmina po wybudowaniu budynku
Urząd gminy / miasta	gm. Siepraw	wypis i wyrys z planu miejscowego, decyzja o warunkach zabudowy, numer porządkowy budynku
Starostwo powiatowe	powiat myślenicki	pozwolenie na budowę lub zgłoszenie, mapy i wypisy z ewidencji gruntów (w miastach na prawach powiatu – urząd miasta)
Sąd rejonowy	Sąd Rejonowy w Myślenicach	wydział ksiąg wieczystych: księga wieczysta działki, wpis właściciela, hipoteka
Urząd skarbowy	Urząd Skarbowy w Myślenicach	podatek PCC przy zakupie (przy umowie u notariusza pobiera go notariusz), zgłoszenie spadku lub darowizny
Nadleśnictwo	Nadleśnictwo Myślenice	gdy w pobliżu jest las państwowy (sąsiedztwo lasu, drogi leśne); lasy prywatne nadzoruje zwykle starosta
Wody Polskie	Zarząd Zlewni w Krakowie	sprawy wodnoprawne – zgłoszenie lub pozwolenie np. przy studni, przydomowej oczyszczalni, drenażu, rowie (czy potrzebne – zależy od rodzaju i wielkości urządzenia)

Dane: państwowy rejestr granic PRG (GUGiK), pobrano 27.10.2026. Właściwość urzędu potwierdź na jego stronie internetowej – granice w rejestrze bywają nieaktualne.

Planer działki jest darmowy i bez reklam. Jeśli ten raport Ci pomógł, możesz wesprzeć jego rozwój: buycoffee.to/mateusztworca ☕